


1	2	3	4	5	6	7	8
---	---	---	---	---	---	---	---

SƠ ĐỒ NGUYÊN LÝ TRẠM PHÂN PHỐI

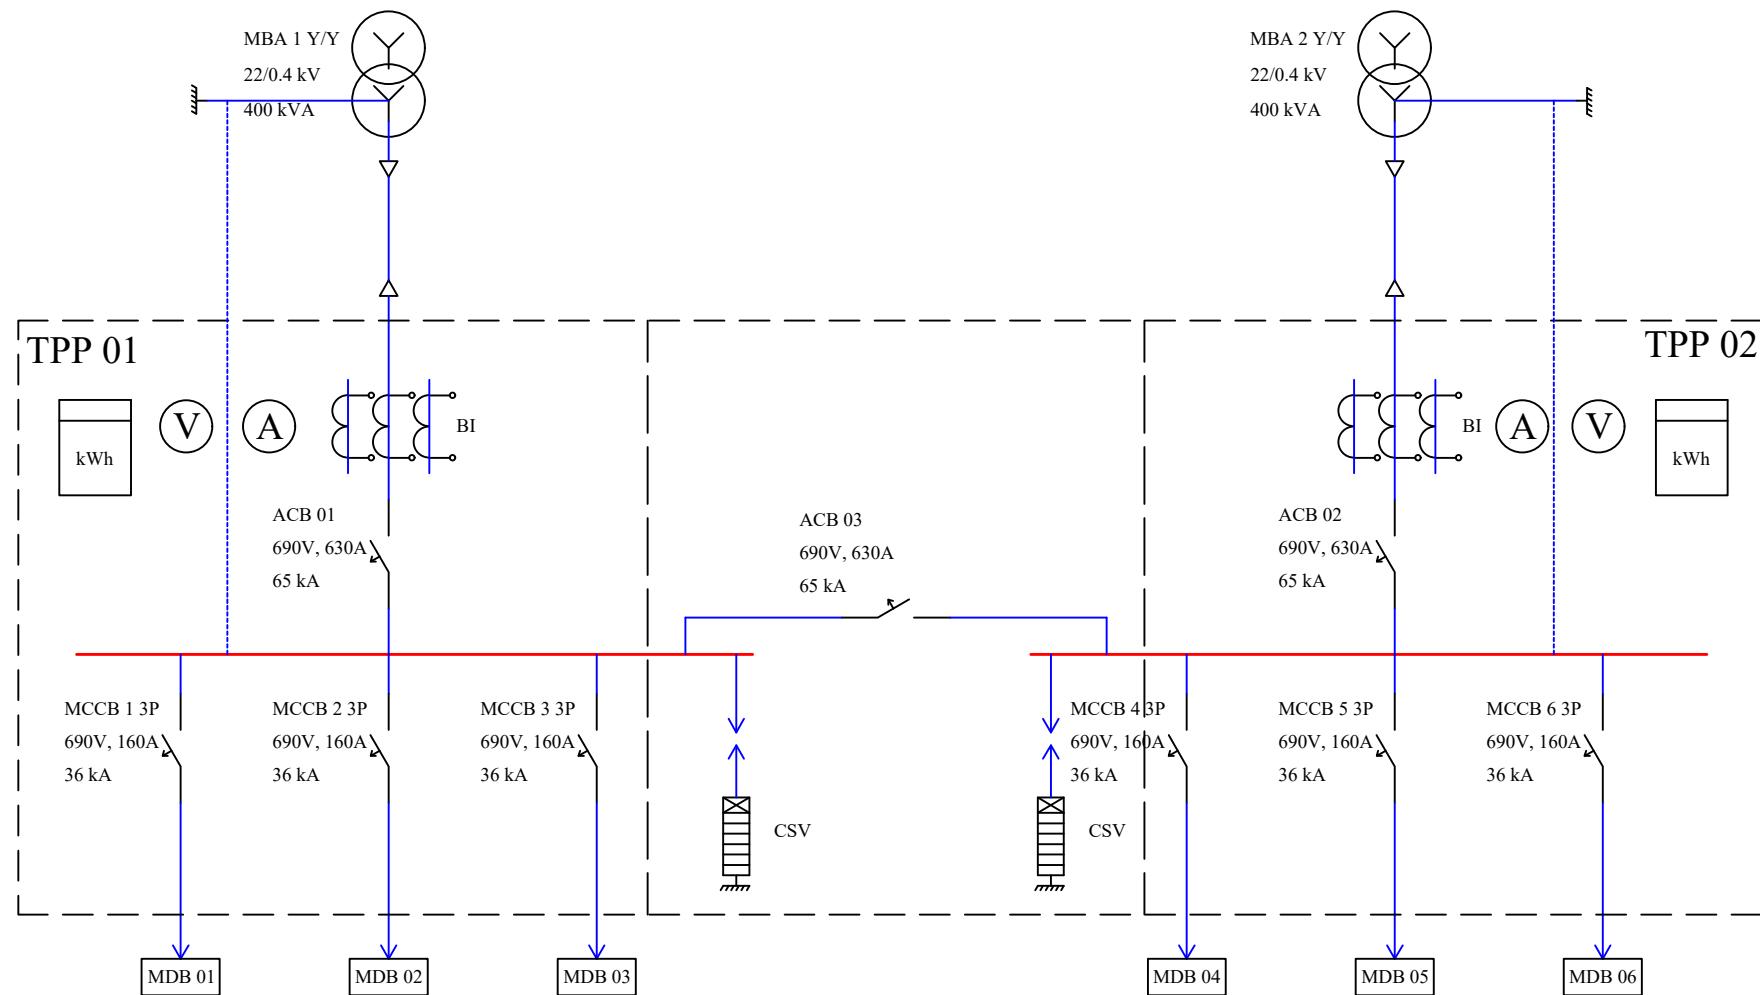

CLIENT	VENDOR	NOTE:	NAME	DATE	TITLE: DISTRIBUTION STATION PRINCIPLE
			DESIGNED BY	Pham Viet Tung	
		CHECKED BY			
		APPROVED BY			PAGE: 1 TOTAL: 10 SCALE: 1:1

1

2

3





4

5

6

7


8

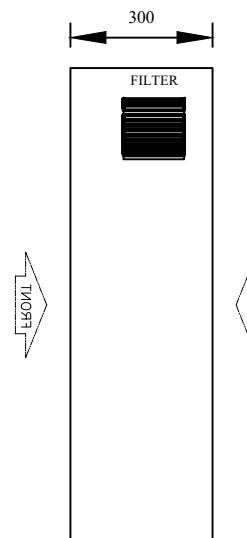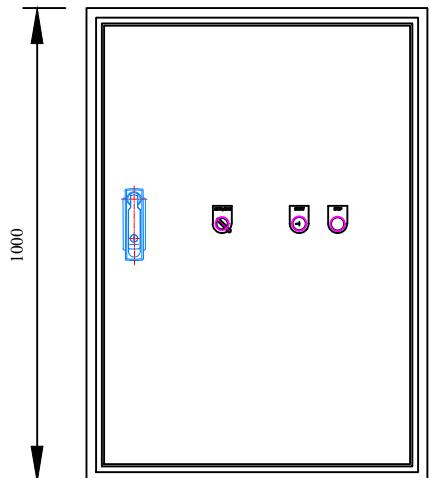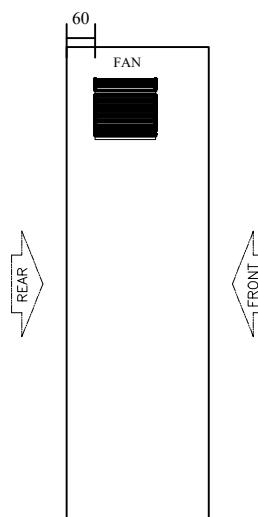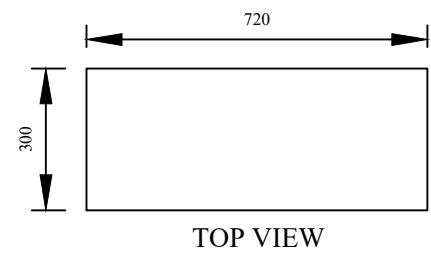




FRONT VIEW

CLIENT	VENDOR	NOTE:	DESIGNED BY	NAME	DATE	TITLE: EXTERNAL LAYOUT						
						CHECKED BY	APPROVED BY	PAGE:	2	TOTAL:	10	SCALE:
				Pham Viet Tung	1/1/2026							

1 2 3 4 5 6 7 8

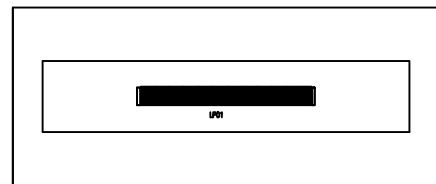


TOP VIEW

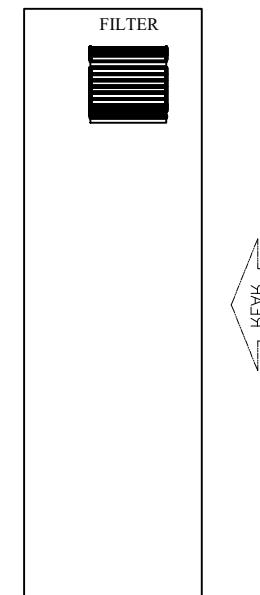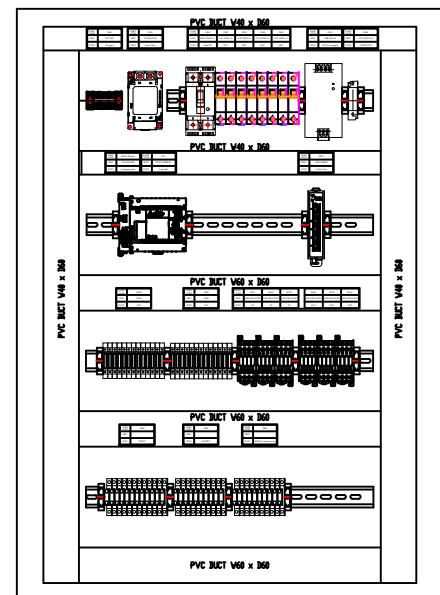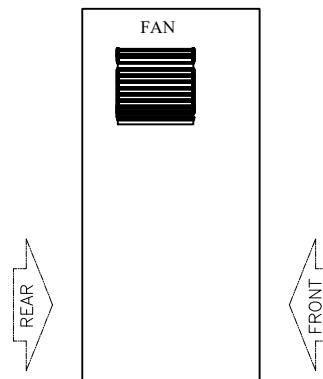


FRONT VIEW

		NOTE:		NAME	DATE	TITLE: INTERNAL LAYOUT					
			DESIGNED BY	Pham Viet Tung	2/1/2026						
			CHECKED BY								
CLIENT	VENDOR		APPROVED BY			PAGE:	3	TOTAL:	10	SCALE:	1:1

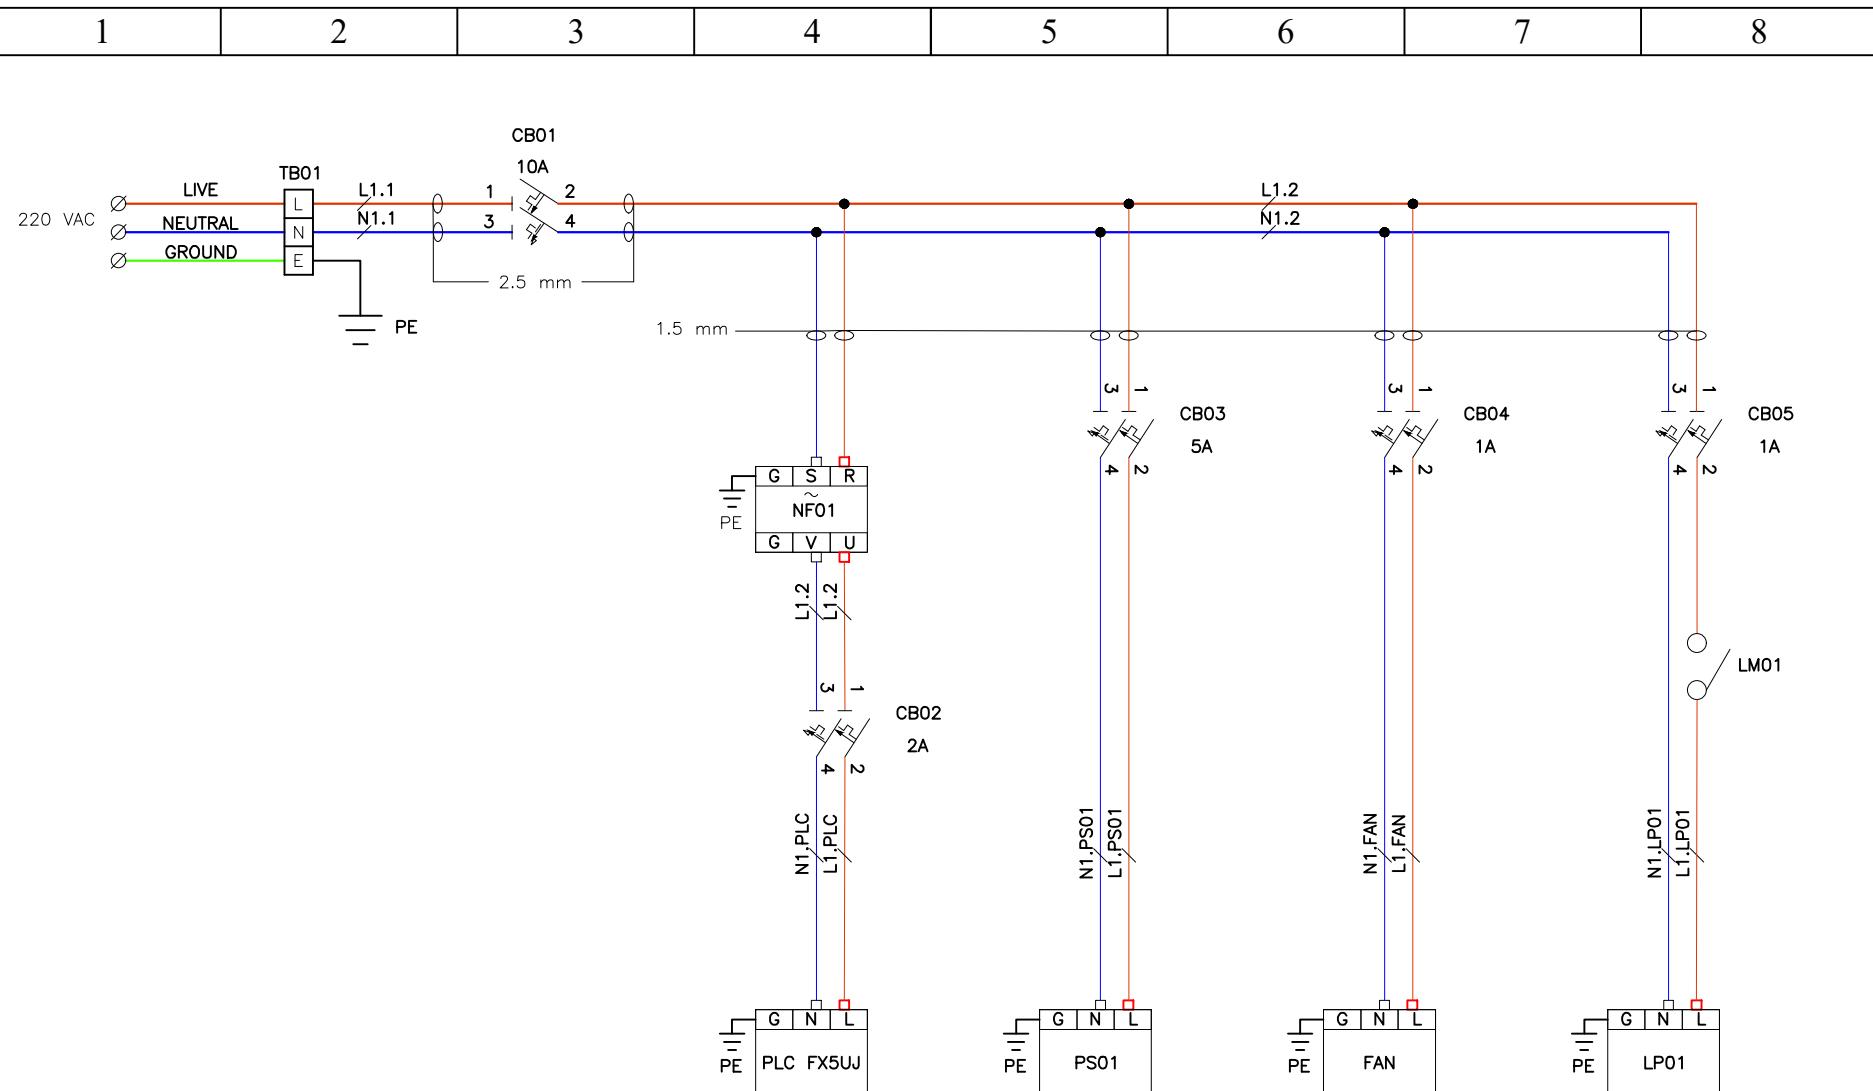


CLIENT	VENDOR	NOTE:	NAME	DATE	TITLE: AC POWER DISTRIBUTION			
			DESIGNED BY	02/01/2026				
		CHECKED BY						
		APPROVED BY			PAGE:	4	TOTAL:	10
					SCALE:	1:1		

1	2	3	4	5	6	7	8
---	---	---	---	---	---	---	---

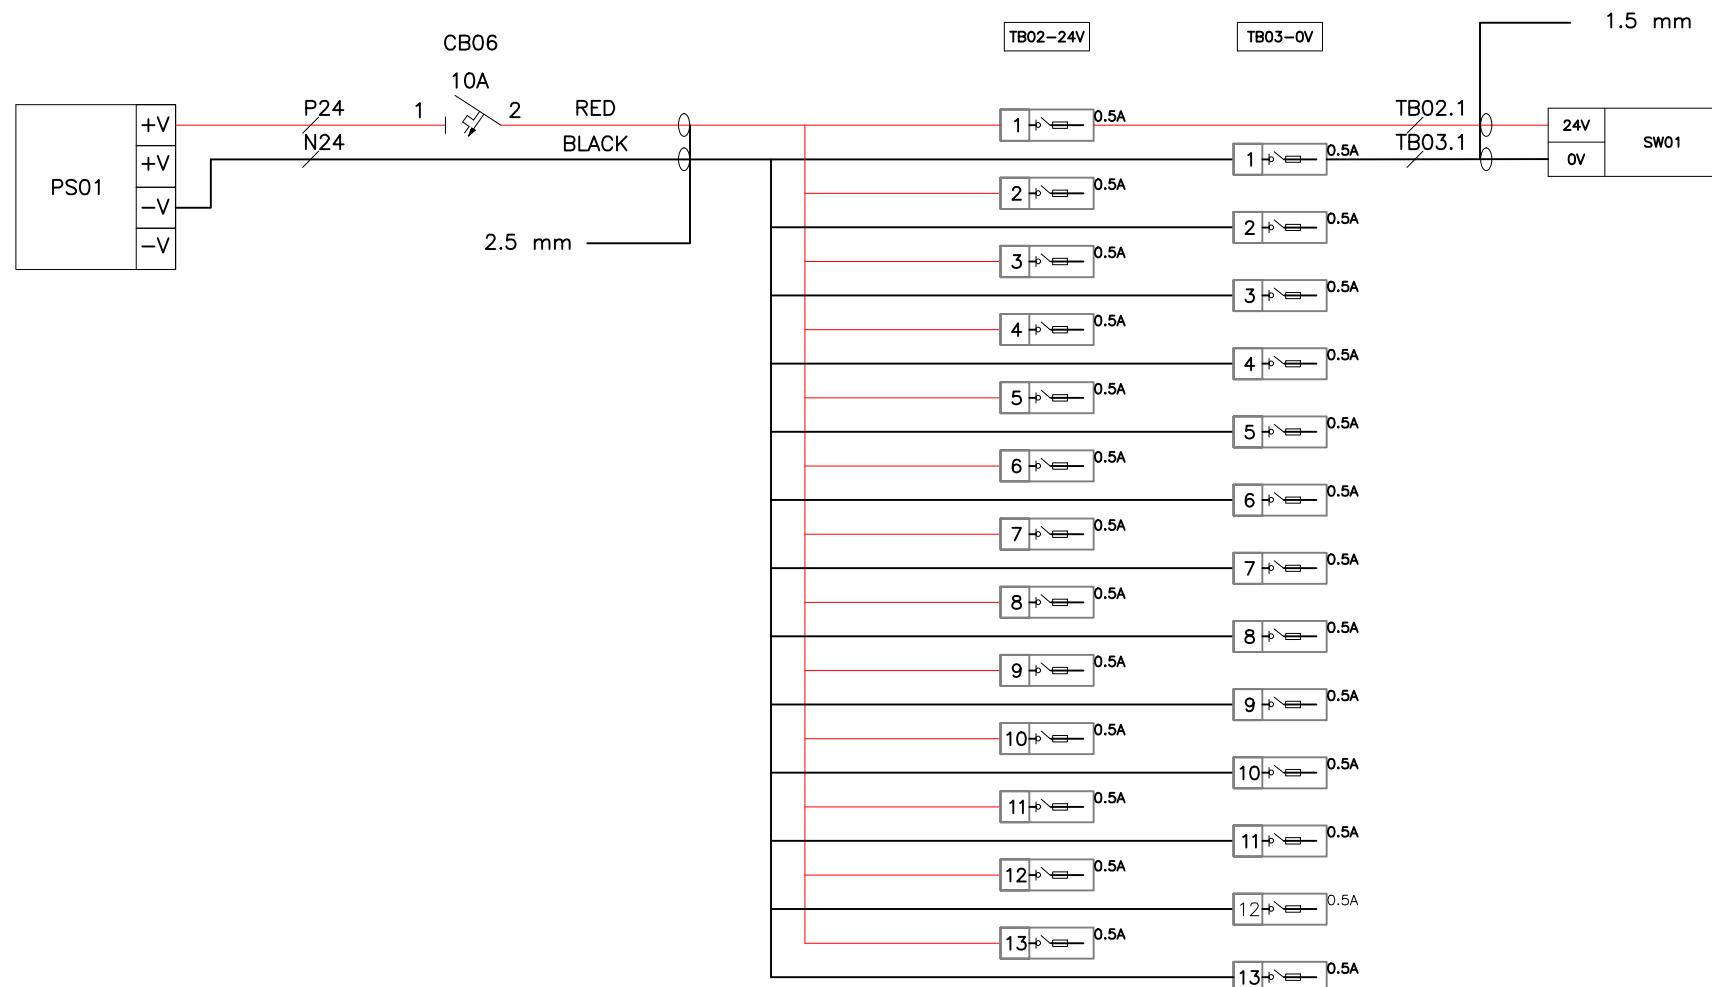

CLIENT	VENDOR	NOTE:	NAME	DATE	TITLE: DC POWER DISTRIBUTION
			DESIGNED BY Pham Viet Tung	02/01/2026	
			CHECKED BY		
			APPROVED BY		
			PAGE:	5	TOTAL: 10 SCALE: 1:1

1 2 3 4 5 6 7 8

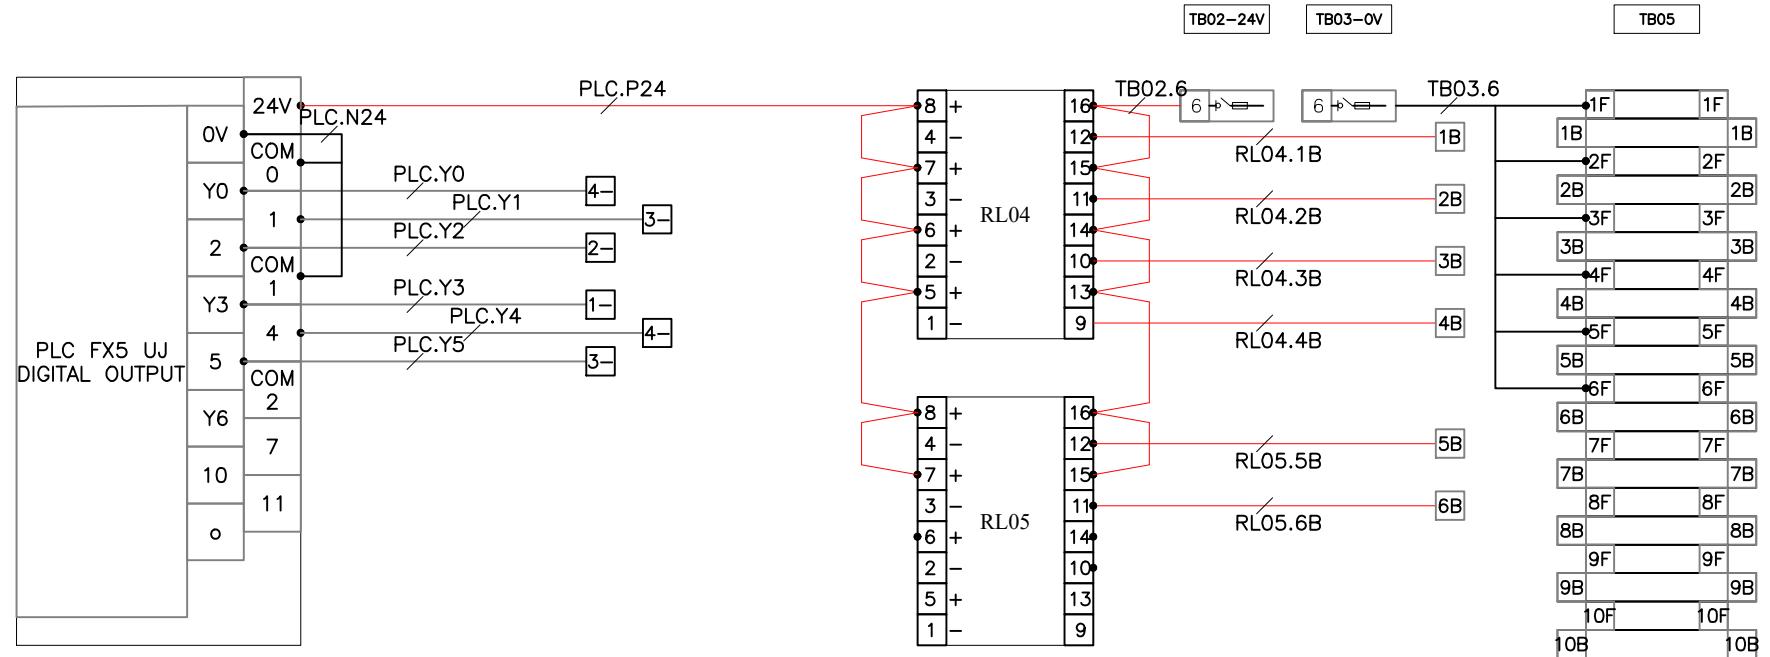

		NOTE:		NAME	DATE	TITLE: OUTPUT WIRING					
			DESIGNED BY	Pham Viet Tung	03/01/2026						
			CHECKED BY								
CLIENT	VENDOR		APPROVED BY			PAGE:	7	TOTAL:	10	SCALE:	1:1

1

2

3




4

5

6


7

8

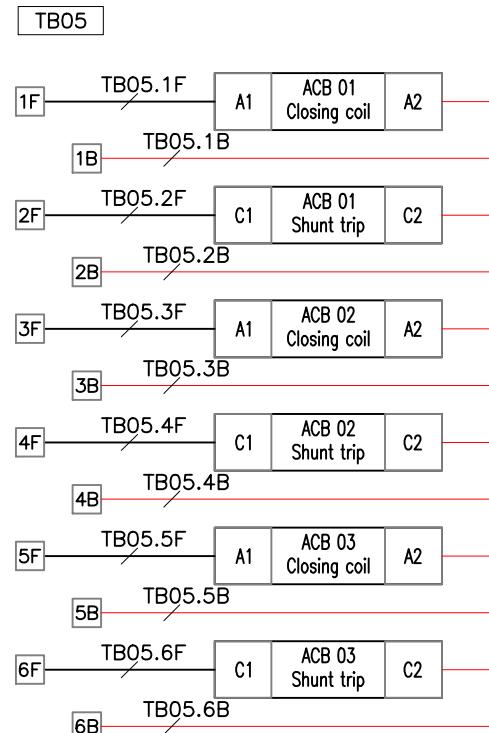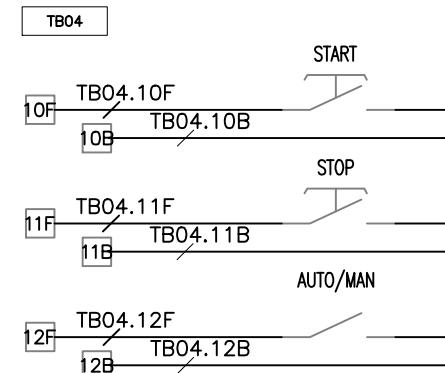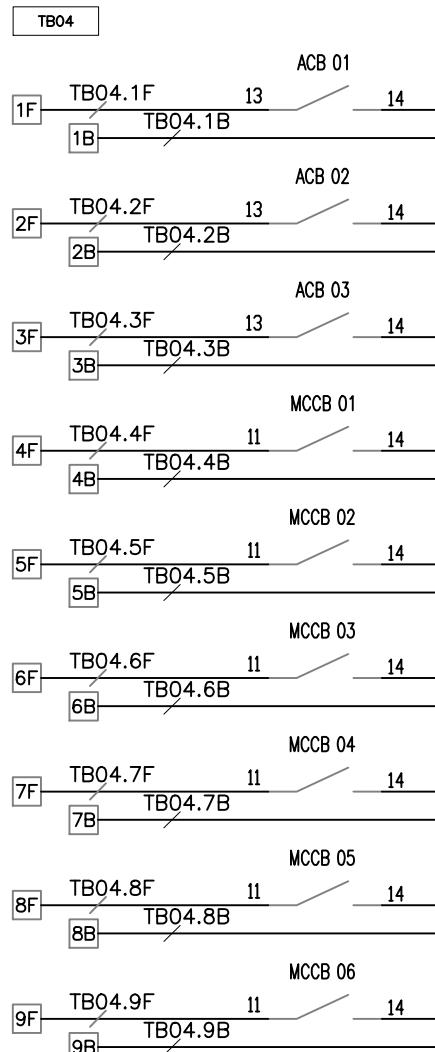

CLIENT	VENDOR	NOTE:	DESIGNED BY	NAME	DATE	TITLE:				
						INPUT/OUTPUT TERMINAL TO DEVICES				
			CHECKED BY			PAGE:	8	TOTAL:	10	SCALE: 1:1
			APPROVED BY							

1	2	3	4	5	6	7	8
---	---	---	---	---	---	---	---

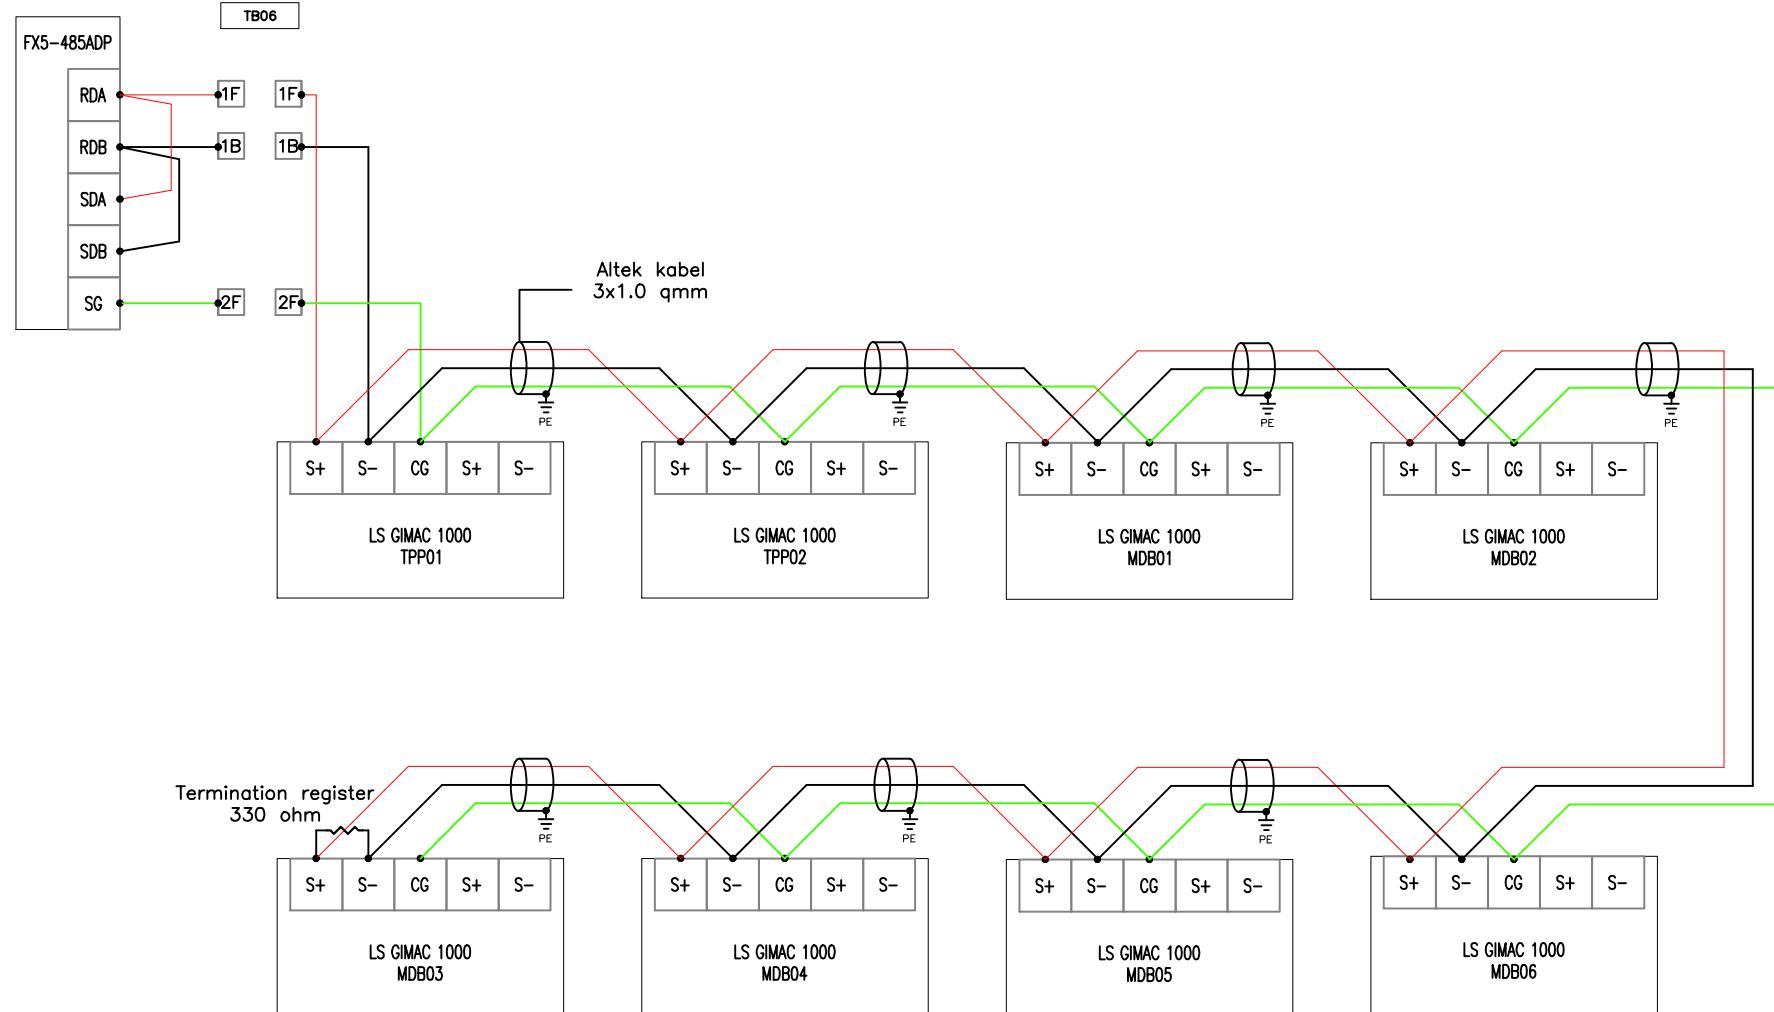

CLIENT	VENDOR	NOTE:	NAME	DATE	TITLE: FX 485ADP TO METERS
			DESIGNED BY	04/01/2026	
			CHECKED BY		
			APPROVED BY		
PAGE:	9	TOTAL:	10	SCALE:	1:1