



SƠ ĐỒ NGUYÊN LÝ TRẠM PHÂN PHỐI

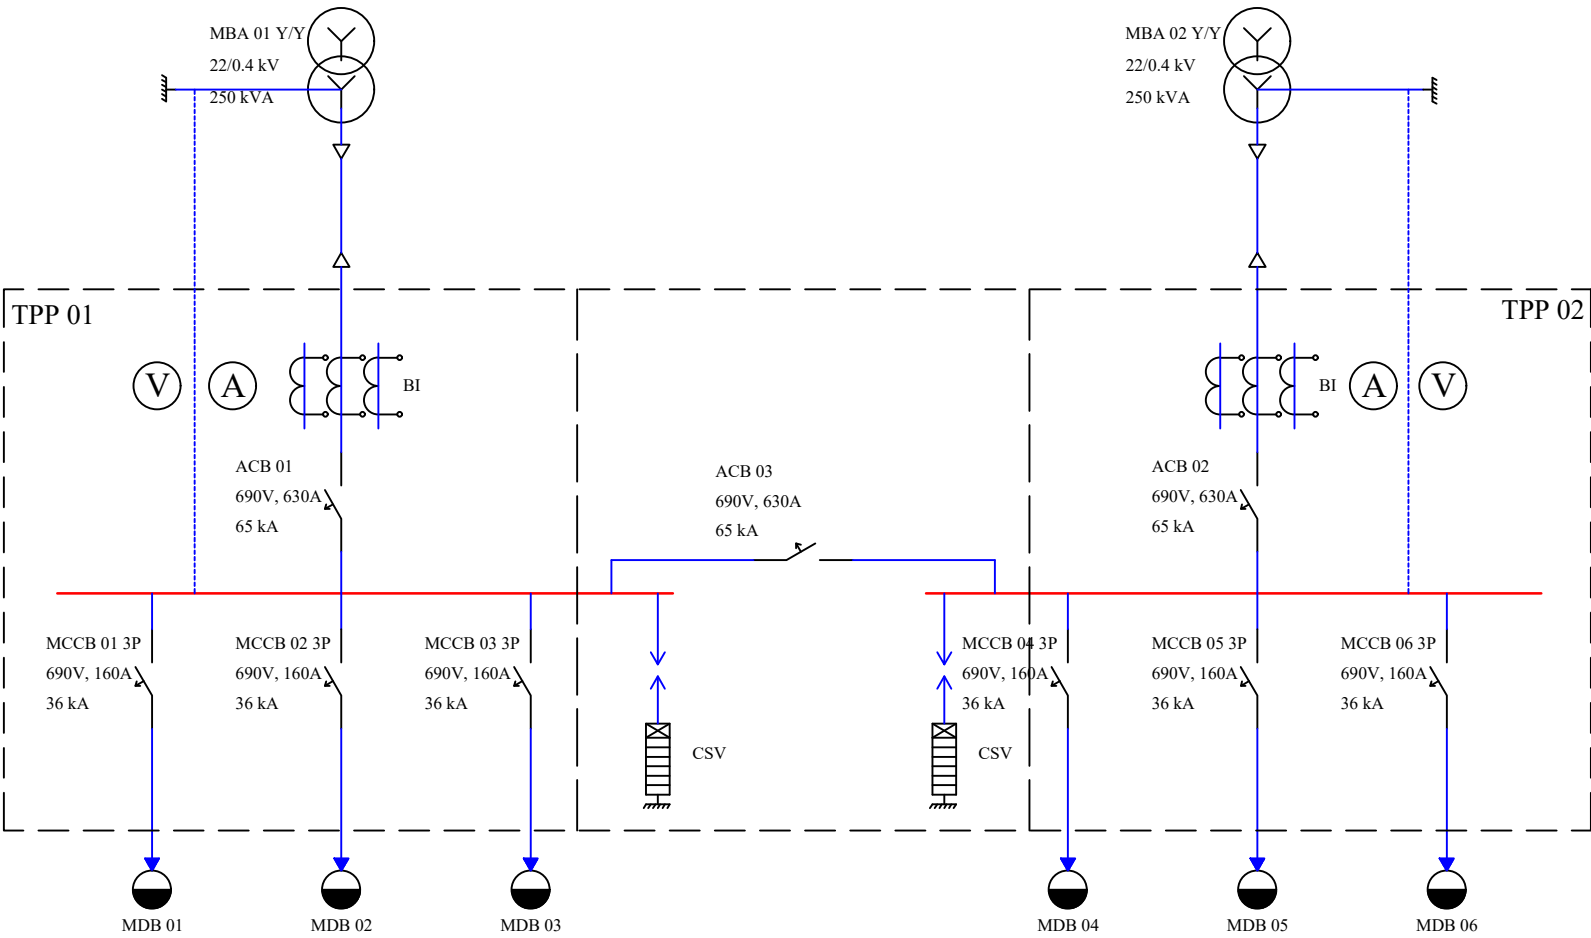


Project name: Uninterruptible Power Supply SCADA on Electricity for an Industrial Plant	Commission	Name	Date time	Drawing name:				
	Designed	PHAM VIET TUNG	2026-01-01	Distribution Station Principle				
	Checked							
	Approved			Page No.	1/10	Scale		Recv A


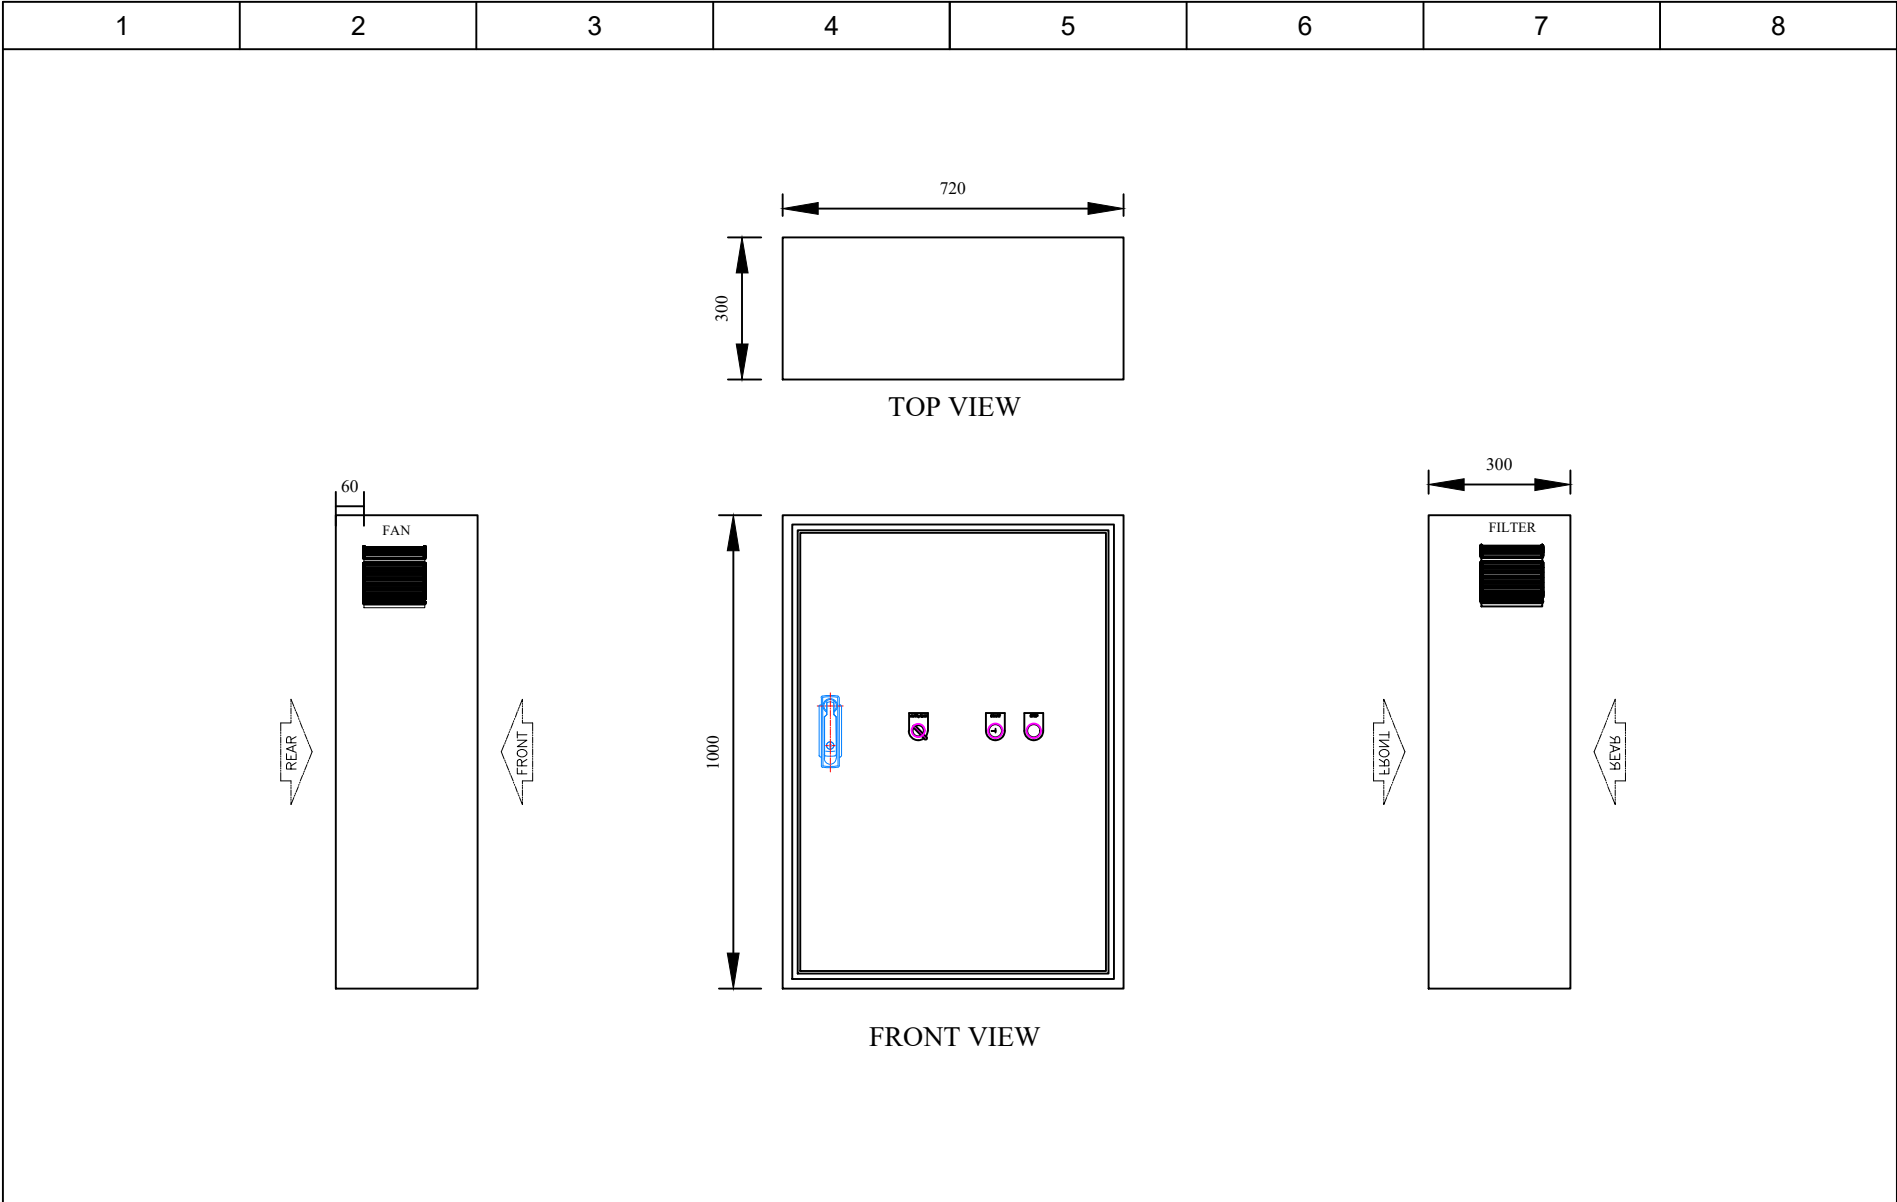


Project name: Uninterruptible Power Supply SCADA on Electricity for an Industrial Plant	Commission	Name	Date time	Drawing name: External Cabinet Layout					
	Designed	PHAM VIET TUNG	2026-01-01						
	Checked								
	Approved			Page No.	2/10	Scale	1:1	Recv	A

1	2	3	4	5	6	7	8
---	---	---	---	---	---	---	---

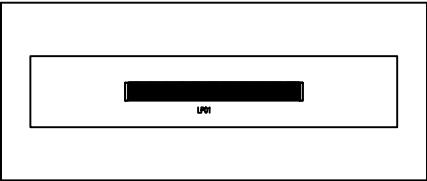


TOP VIEW

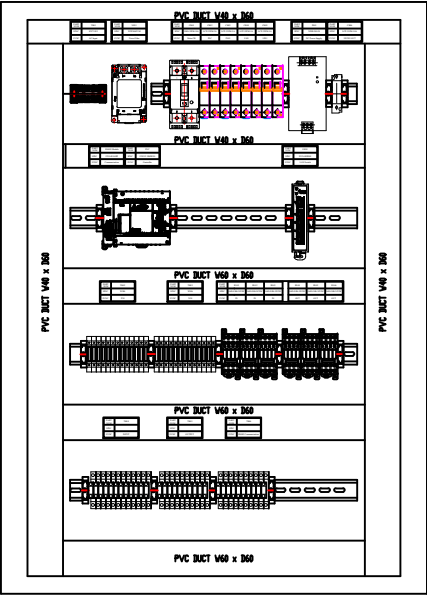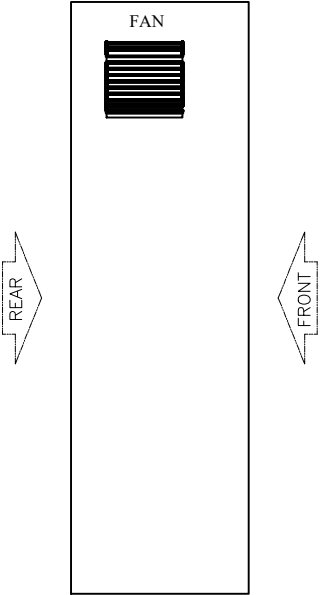


FRONT VIEW


Project name: Uninterruptible Power Supply SCADA on Electricity for an Industrial Plant	Commission	Name	Date time	Drawing name: Internal Cabinet Layout					
	Designed	PHAM VIET TUNG	2026-01-01						
	Checked								
	Approved			Page No.	3/10	Scale	1:1	Recv	A

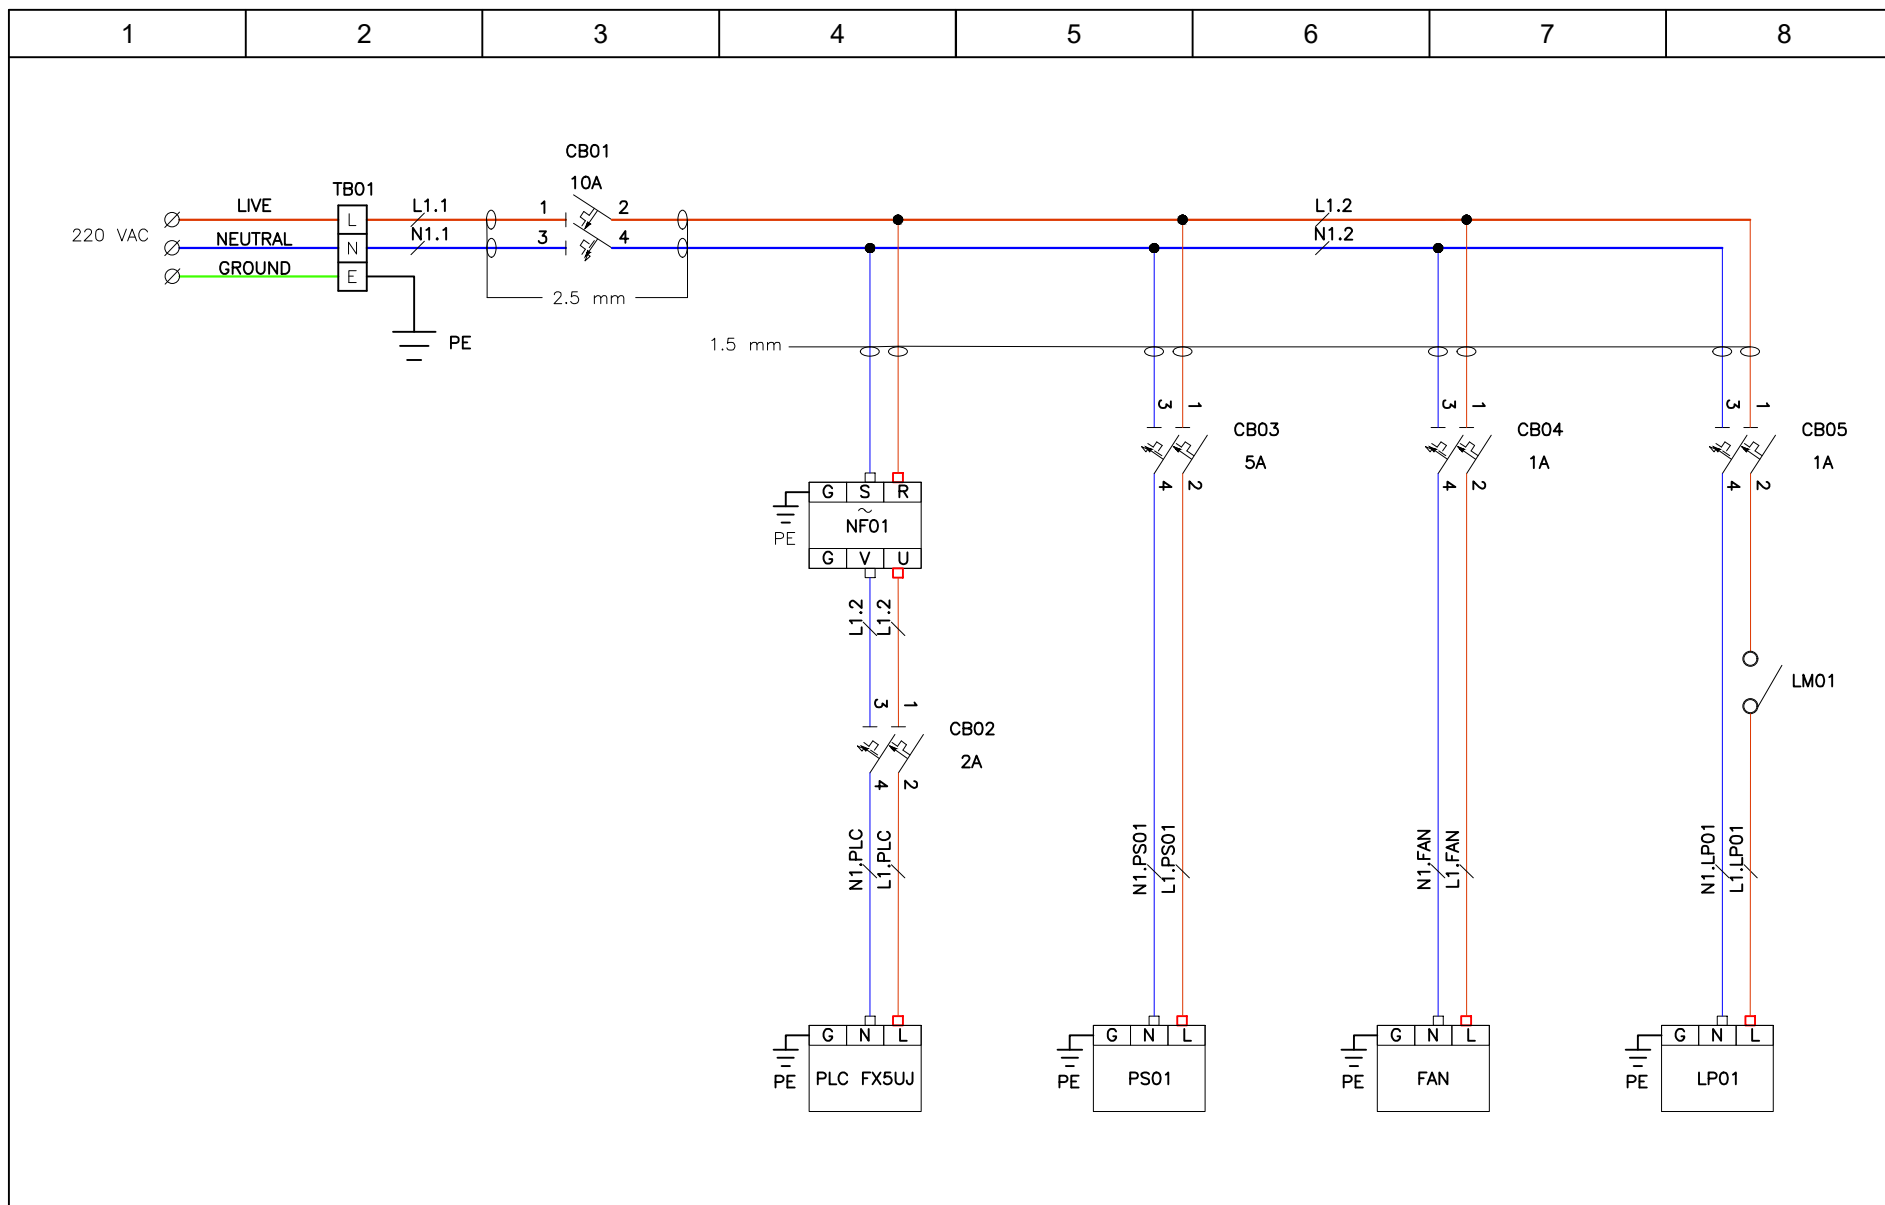


Project name: Uninterruptible Power Supply SCADA on Electricity for an Industrial Plant	Commission	Name	Date time	Drawing name: AC Power Distribution					
	Designed	PHAM VIET TUNG	2026-01-02						
	Checked								
	Approved			Page No.	4/10	Scale		Recv	A

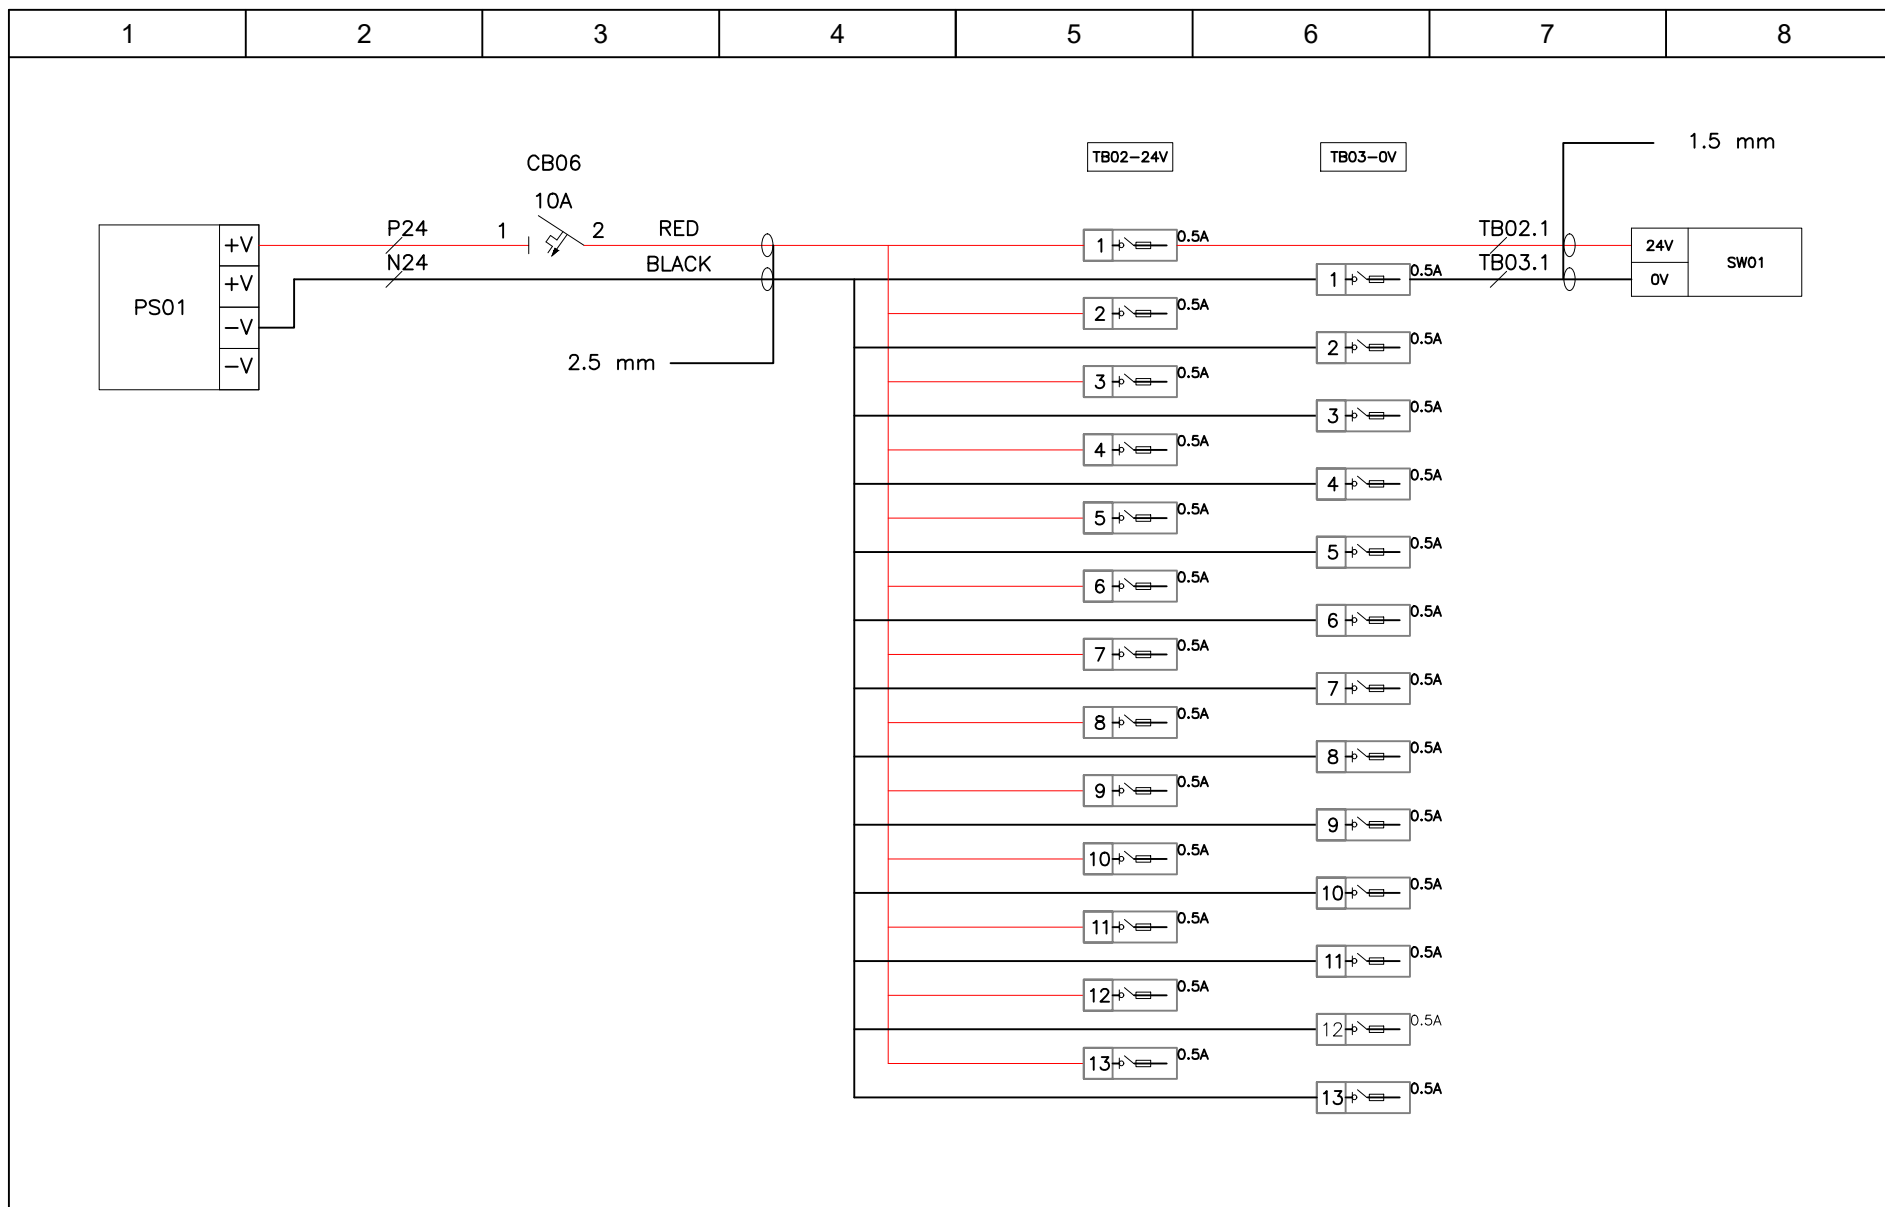


Project name: Uninterruptible Power Supply SCADA on Electricity for an Industrial Plant	Commission	Name	Date time	Drawing name:					
	Designed	PHAM VIET TUNG	2026-01-02	DC Power Distribution					
	Checked								
	Approved			Page No.	5/10	Scale		Recv	A

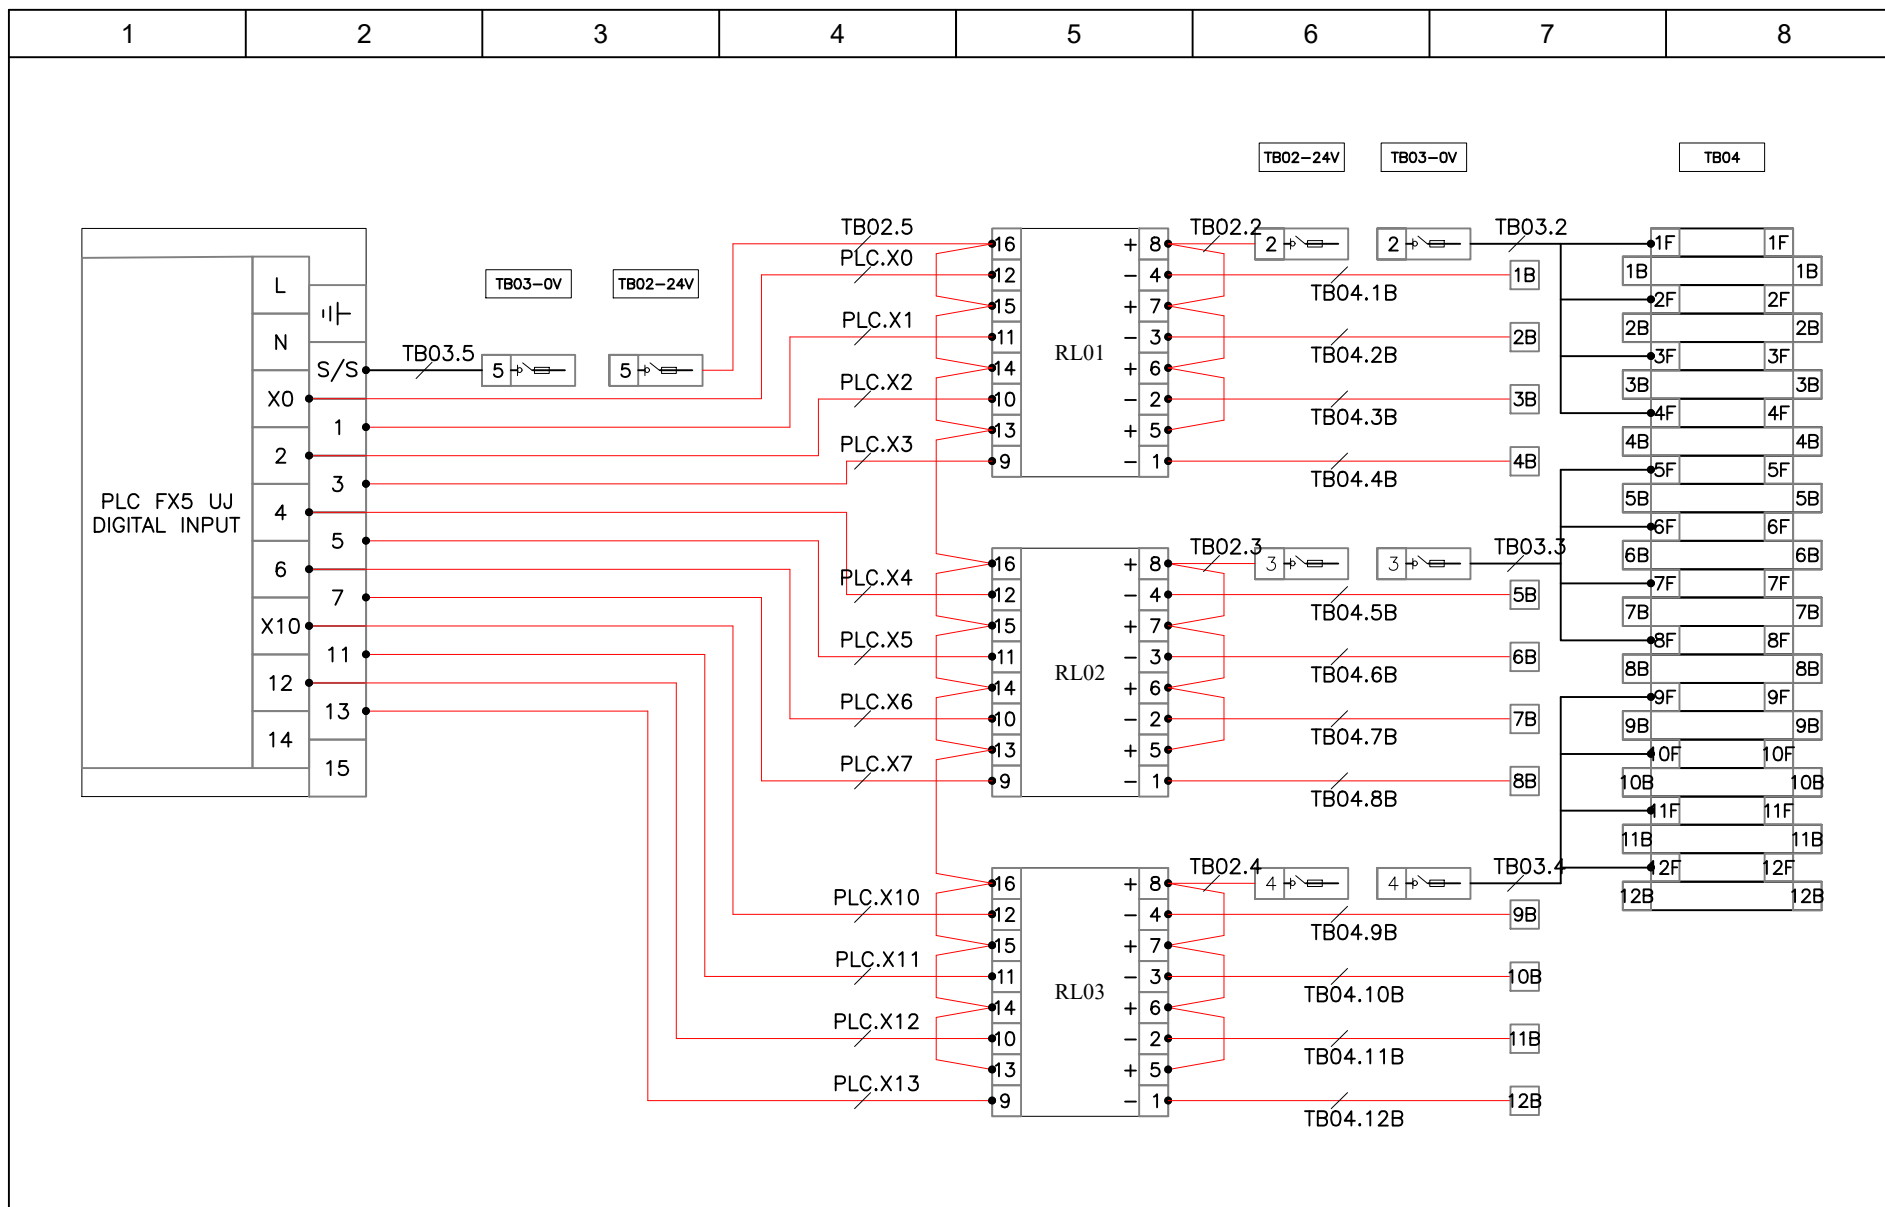


Project name: Uninterruptible Power Supply SCADA on Electricity for an Industrial Plant	Commission	Name	Date time	Drawing name: Input wiring				
	Designed	PHAM VIET TUNG	2026-01-02					
	Checked							
	Approved			Page No.	6/10	Scale	Recv	A

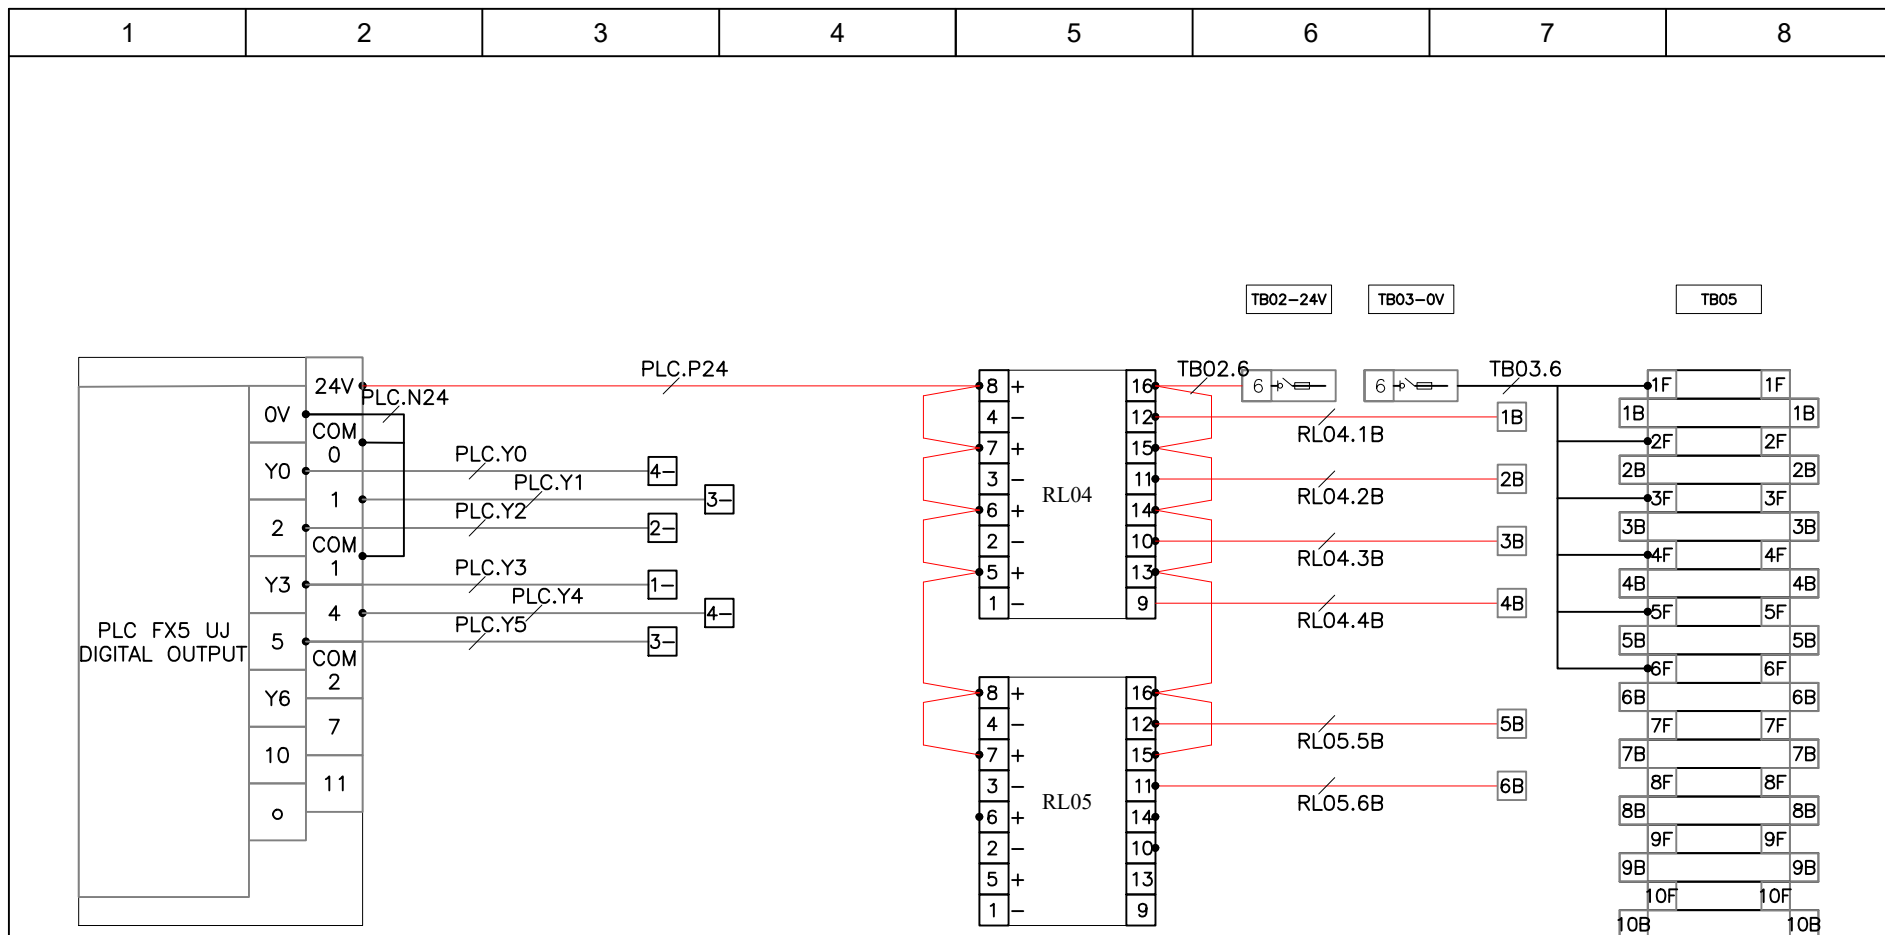

Project name: Uninterruptible Power Supply SCADA on Electricity for an Industrial Plant	Commission	Name	Date time	Drawing name: Output wiring					
	Designed	PHAM VIET TUNG	2026-01-02						
	Checked								
	Approved			Page No.	7/10	Scale		Recv	A

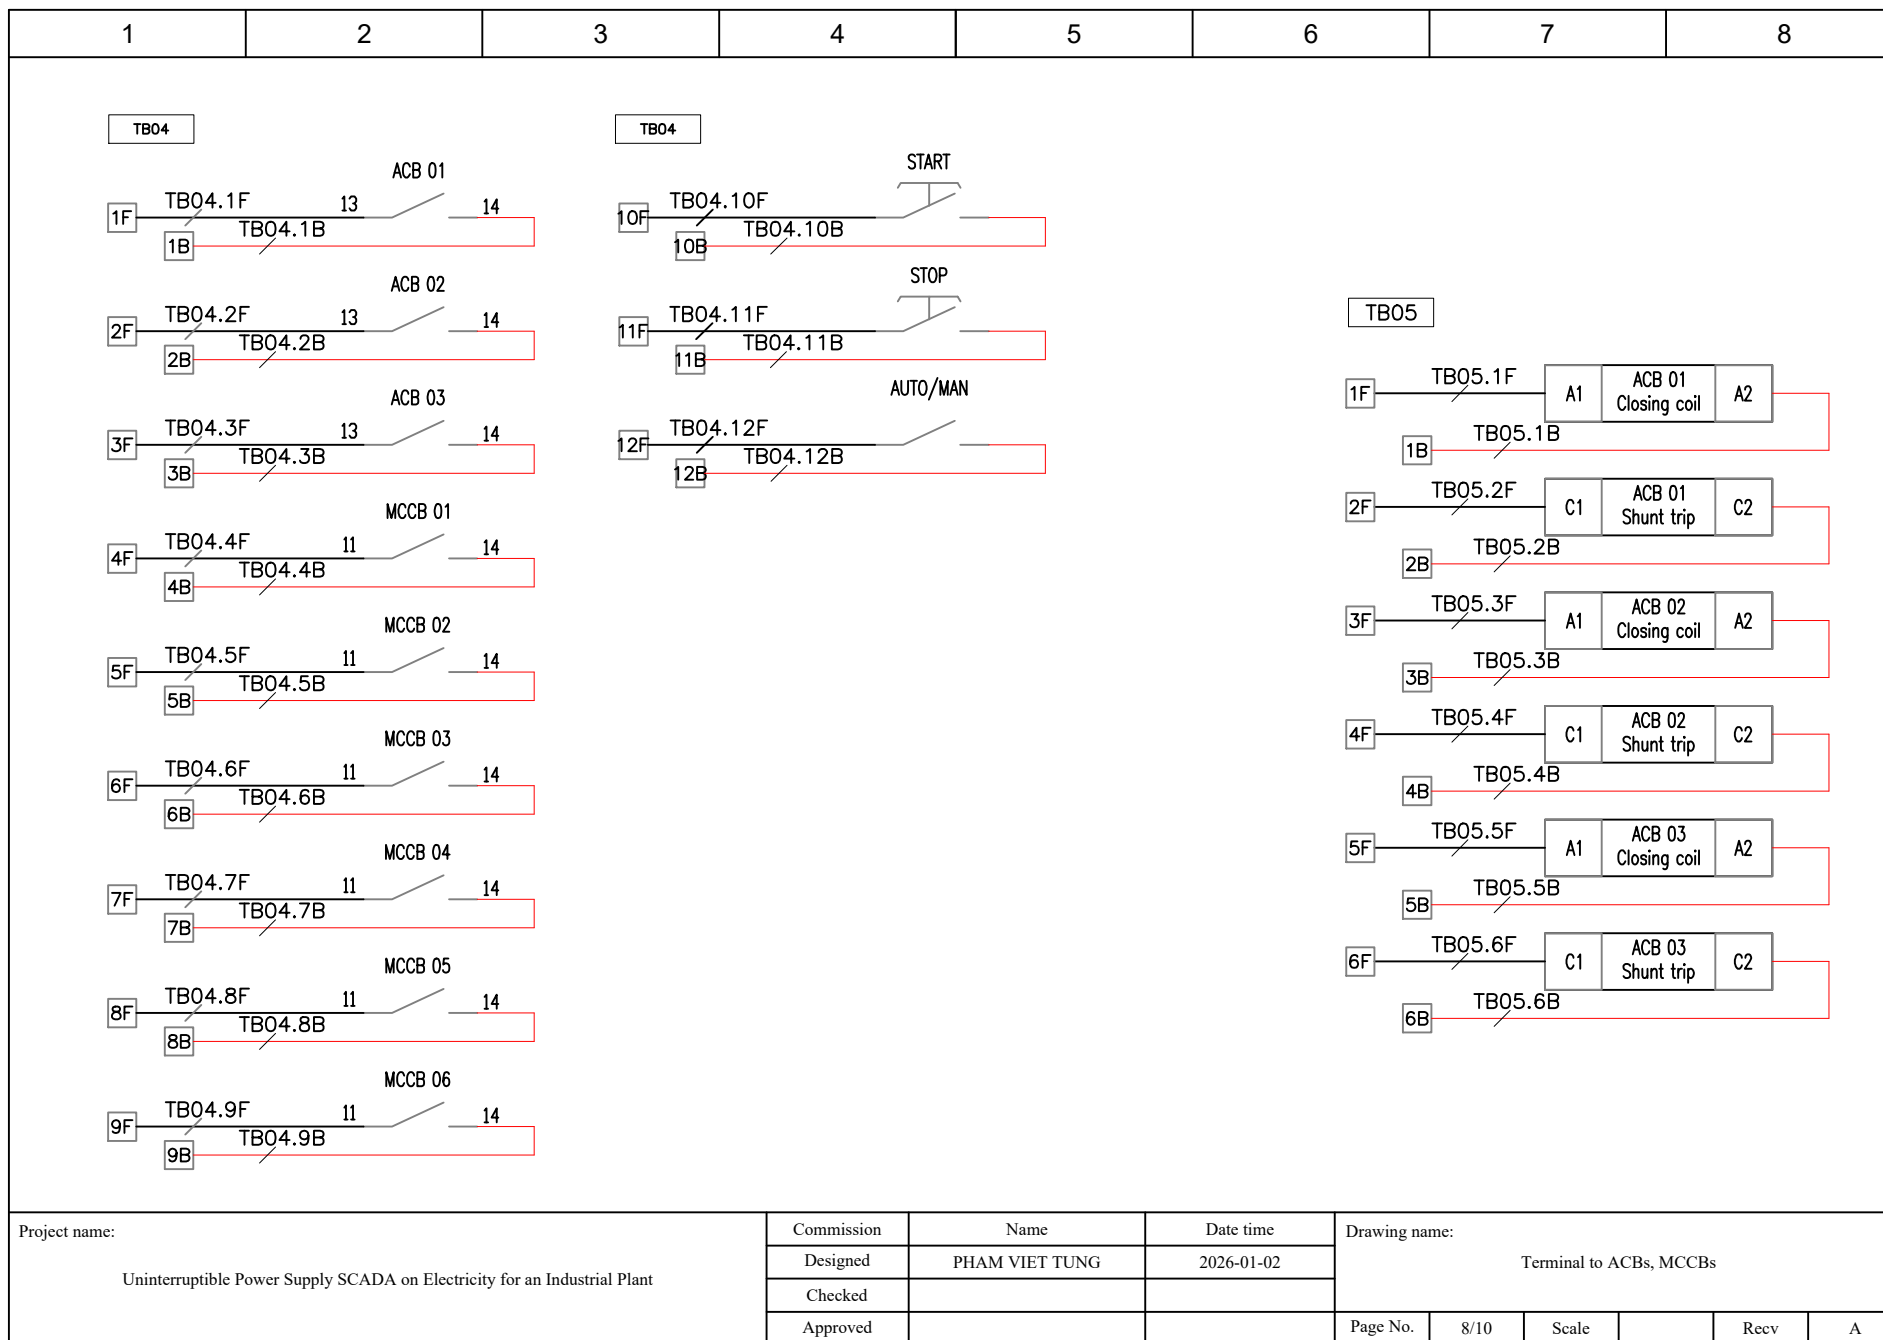

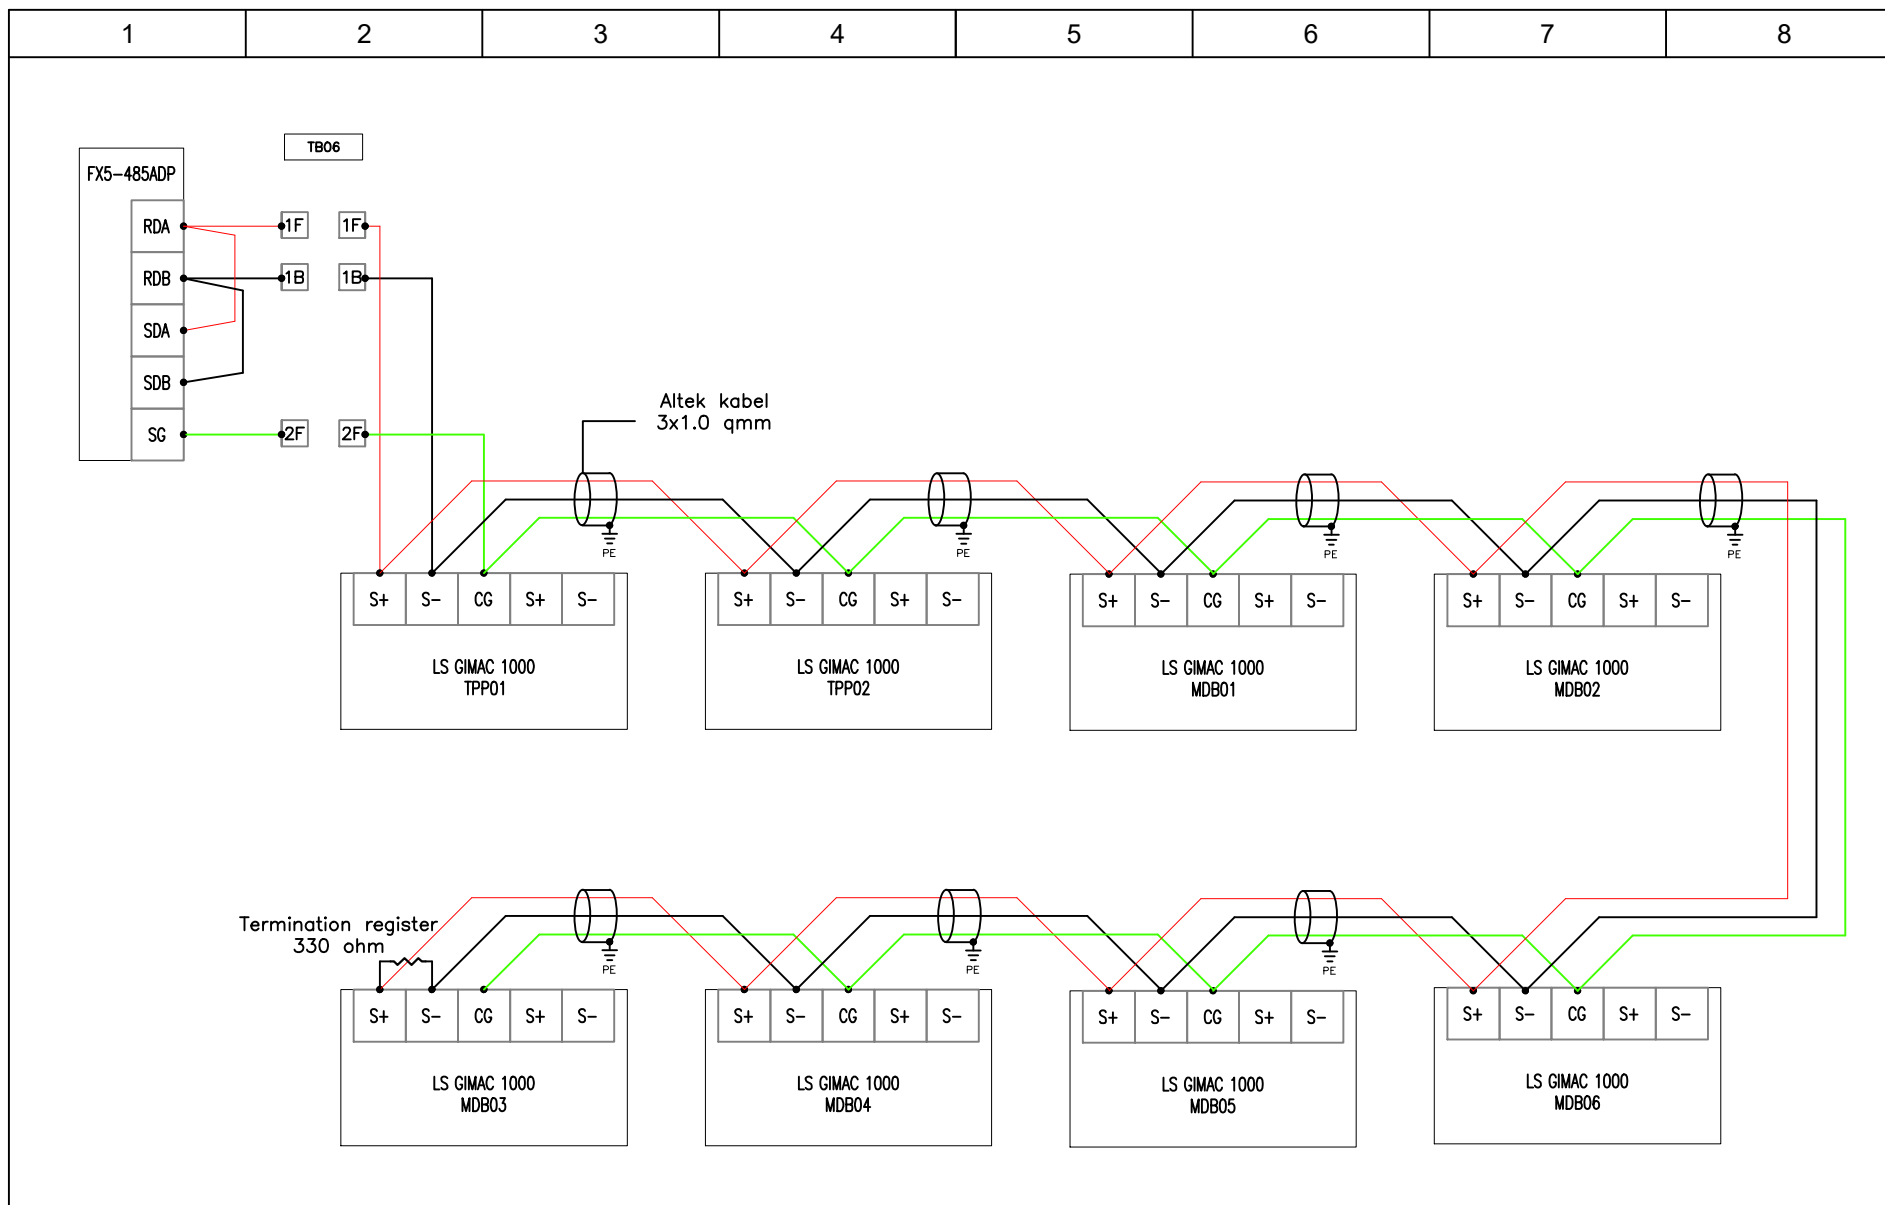

Project name: Uninterruptible Power Supply SCADA on Electricity for an Industrial Plant	Commission	Name	Date time	Drawing name:				
	Designed	PHAM VIET TUNG	2026-01-02	FX-485ADP to Electrical meters				
	Checked							
	Approved			Page No.	9/10	Scale	Recv	A

1	2	3	4	5	6	7	8
---	---	---	---	---	---	---	---

#	Section	Name	Symbol	Model	Spec	Quantity	Manufacturer
1		NOISE FILTER	NF01	WYFS06T1M	6A	1	Woonyoung
2		MAIN CIRCUIT BREAKER	CB01	EBS-32Fb-10A	230 VAC 10A	1	LS
3		CB FOR PLC	CB02	LCP-32FM-2A	2A	1	LS
4		CB FOR 24V POWER SUPPLY	CB03	LCP-32FM-5A	5A	1	LS
5		CB FOR CABINET FAN AND LIGHT	CB04, CB05	LCP-32FM-1A	1A	2	LS
6		DC Power Supply	PS01	NDR-240-24	240VAC TO 24VDC	1	-
7		CB FOR POWER SUPPLY	CB06	LCP-31FM-10A	10A	1	T
8		PLC FX5UJ MITSUBISHI	PLC	FX5UJ 24MR/ES	-	1	mitsubishi
9		RS-485 COMMUNICATION MODULE	RS485 Module	FX5-485 ADP	-	1	mitsubishi
10		LAN Switch	SW01	DVS-005R00	-	1	DELTA
11		FUSE P24, N24	TB02, TB03	WSI6	0.5A	26	-
12		RELAY FOR INPUT	RL01, RL02, RL03	G6D-F4B-24VDC	-	3	OMRON
13		RELAY FOR OUT PUT	RL04, RL05, RL06	G6D-F4B-24VDC	-	3	OMRON
14		TERMINAL BLOCK FOR INPUT	TB04	-	-	12	-
15		TERMINAL BLOCK FOR OUTPUT	TB05	-	-	10	-
16		TERMINAL BLOCK FOR RS485 MODULE	TB06	-	-	10	-
17		START BUTTON					
18		STOP BUTTON					
19		MANUAL/AUTO SWITCH					

Project name: Uninterruptible Power Supply SCADA on Electricity for an Industrial Plant	Commission	Name	Date time	Drawing name: Path list					
	Designed	PHAM VIET TUNG	2026-01-02						
	Checked								
	Approved			Page No.	10/10	Scale		Recv	A